

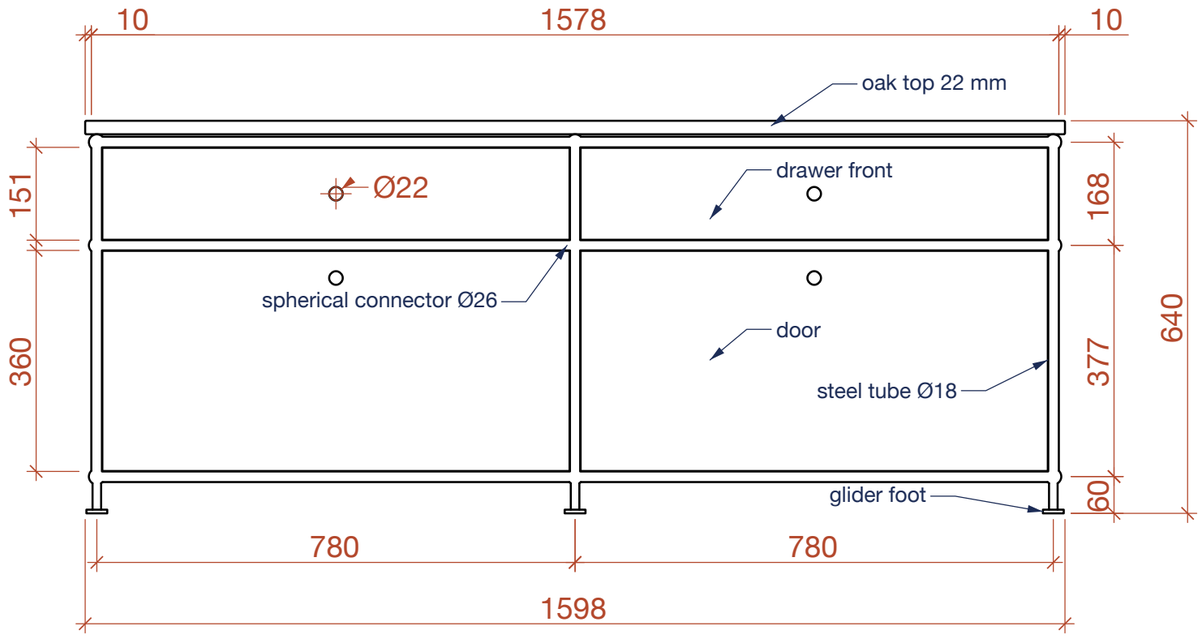


Front elevation 1:10

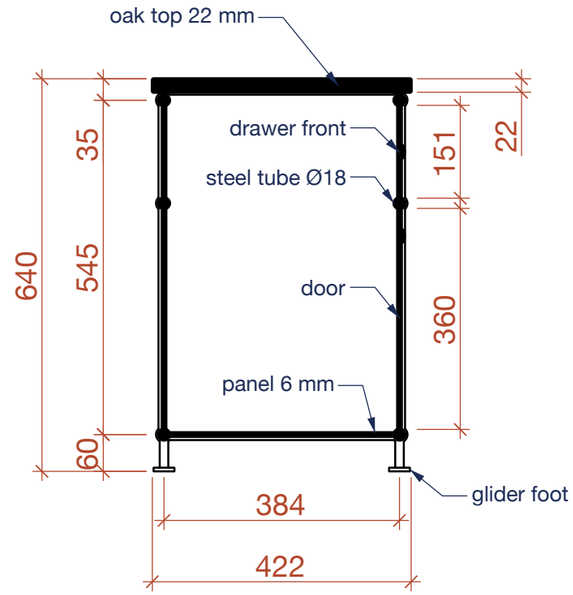

Section A–A 1:10

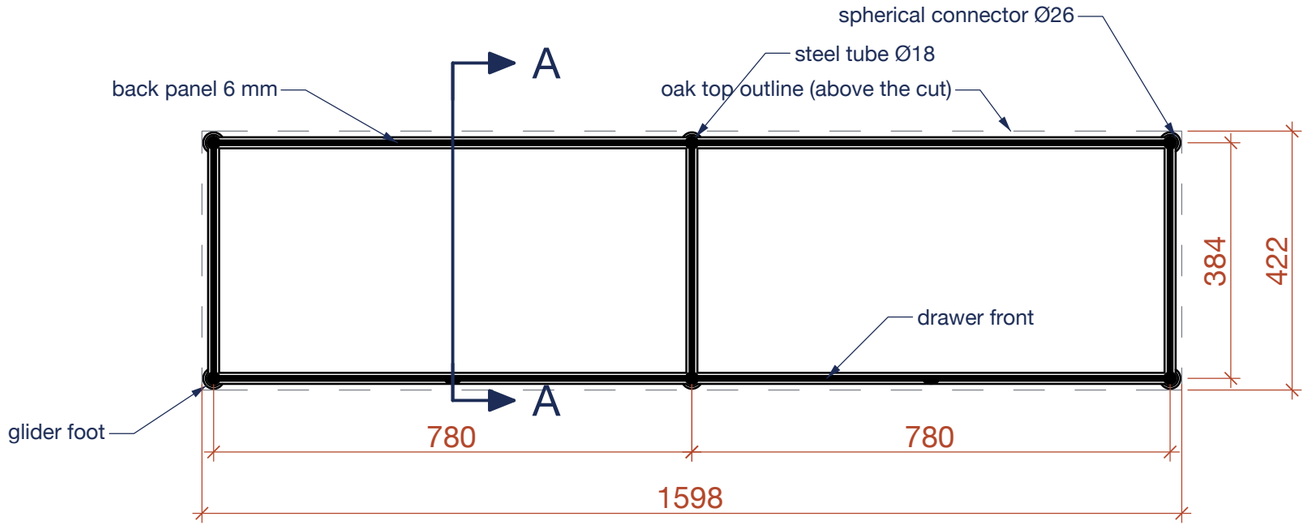

Plan 1:10

Notes

All dimensions in mm.

Section A–A cuts through the middle of bay 1.

Overall 1598 × 422 × 640 mm, two bays of 780 mm.

PROJECT: Modular sideboard				
SHEET TITLE: General arrangement				
SHEET NO.: A-01	SCALE: 1:10	DATE: 2026-10-16	DRAWN BY: RhinoMCP agent	REV.: